


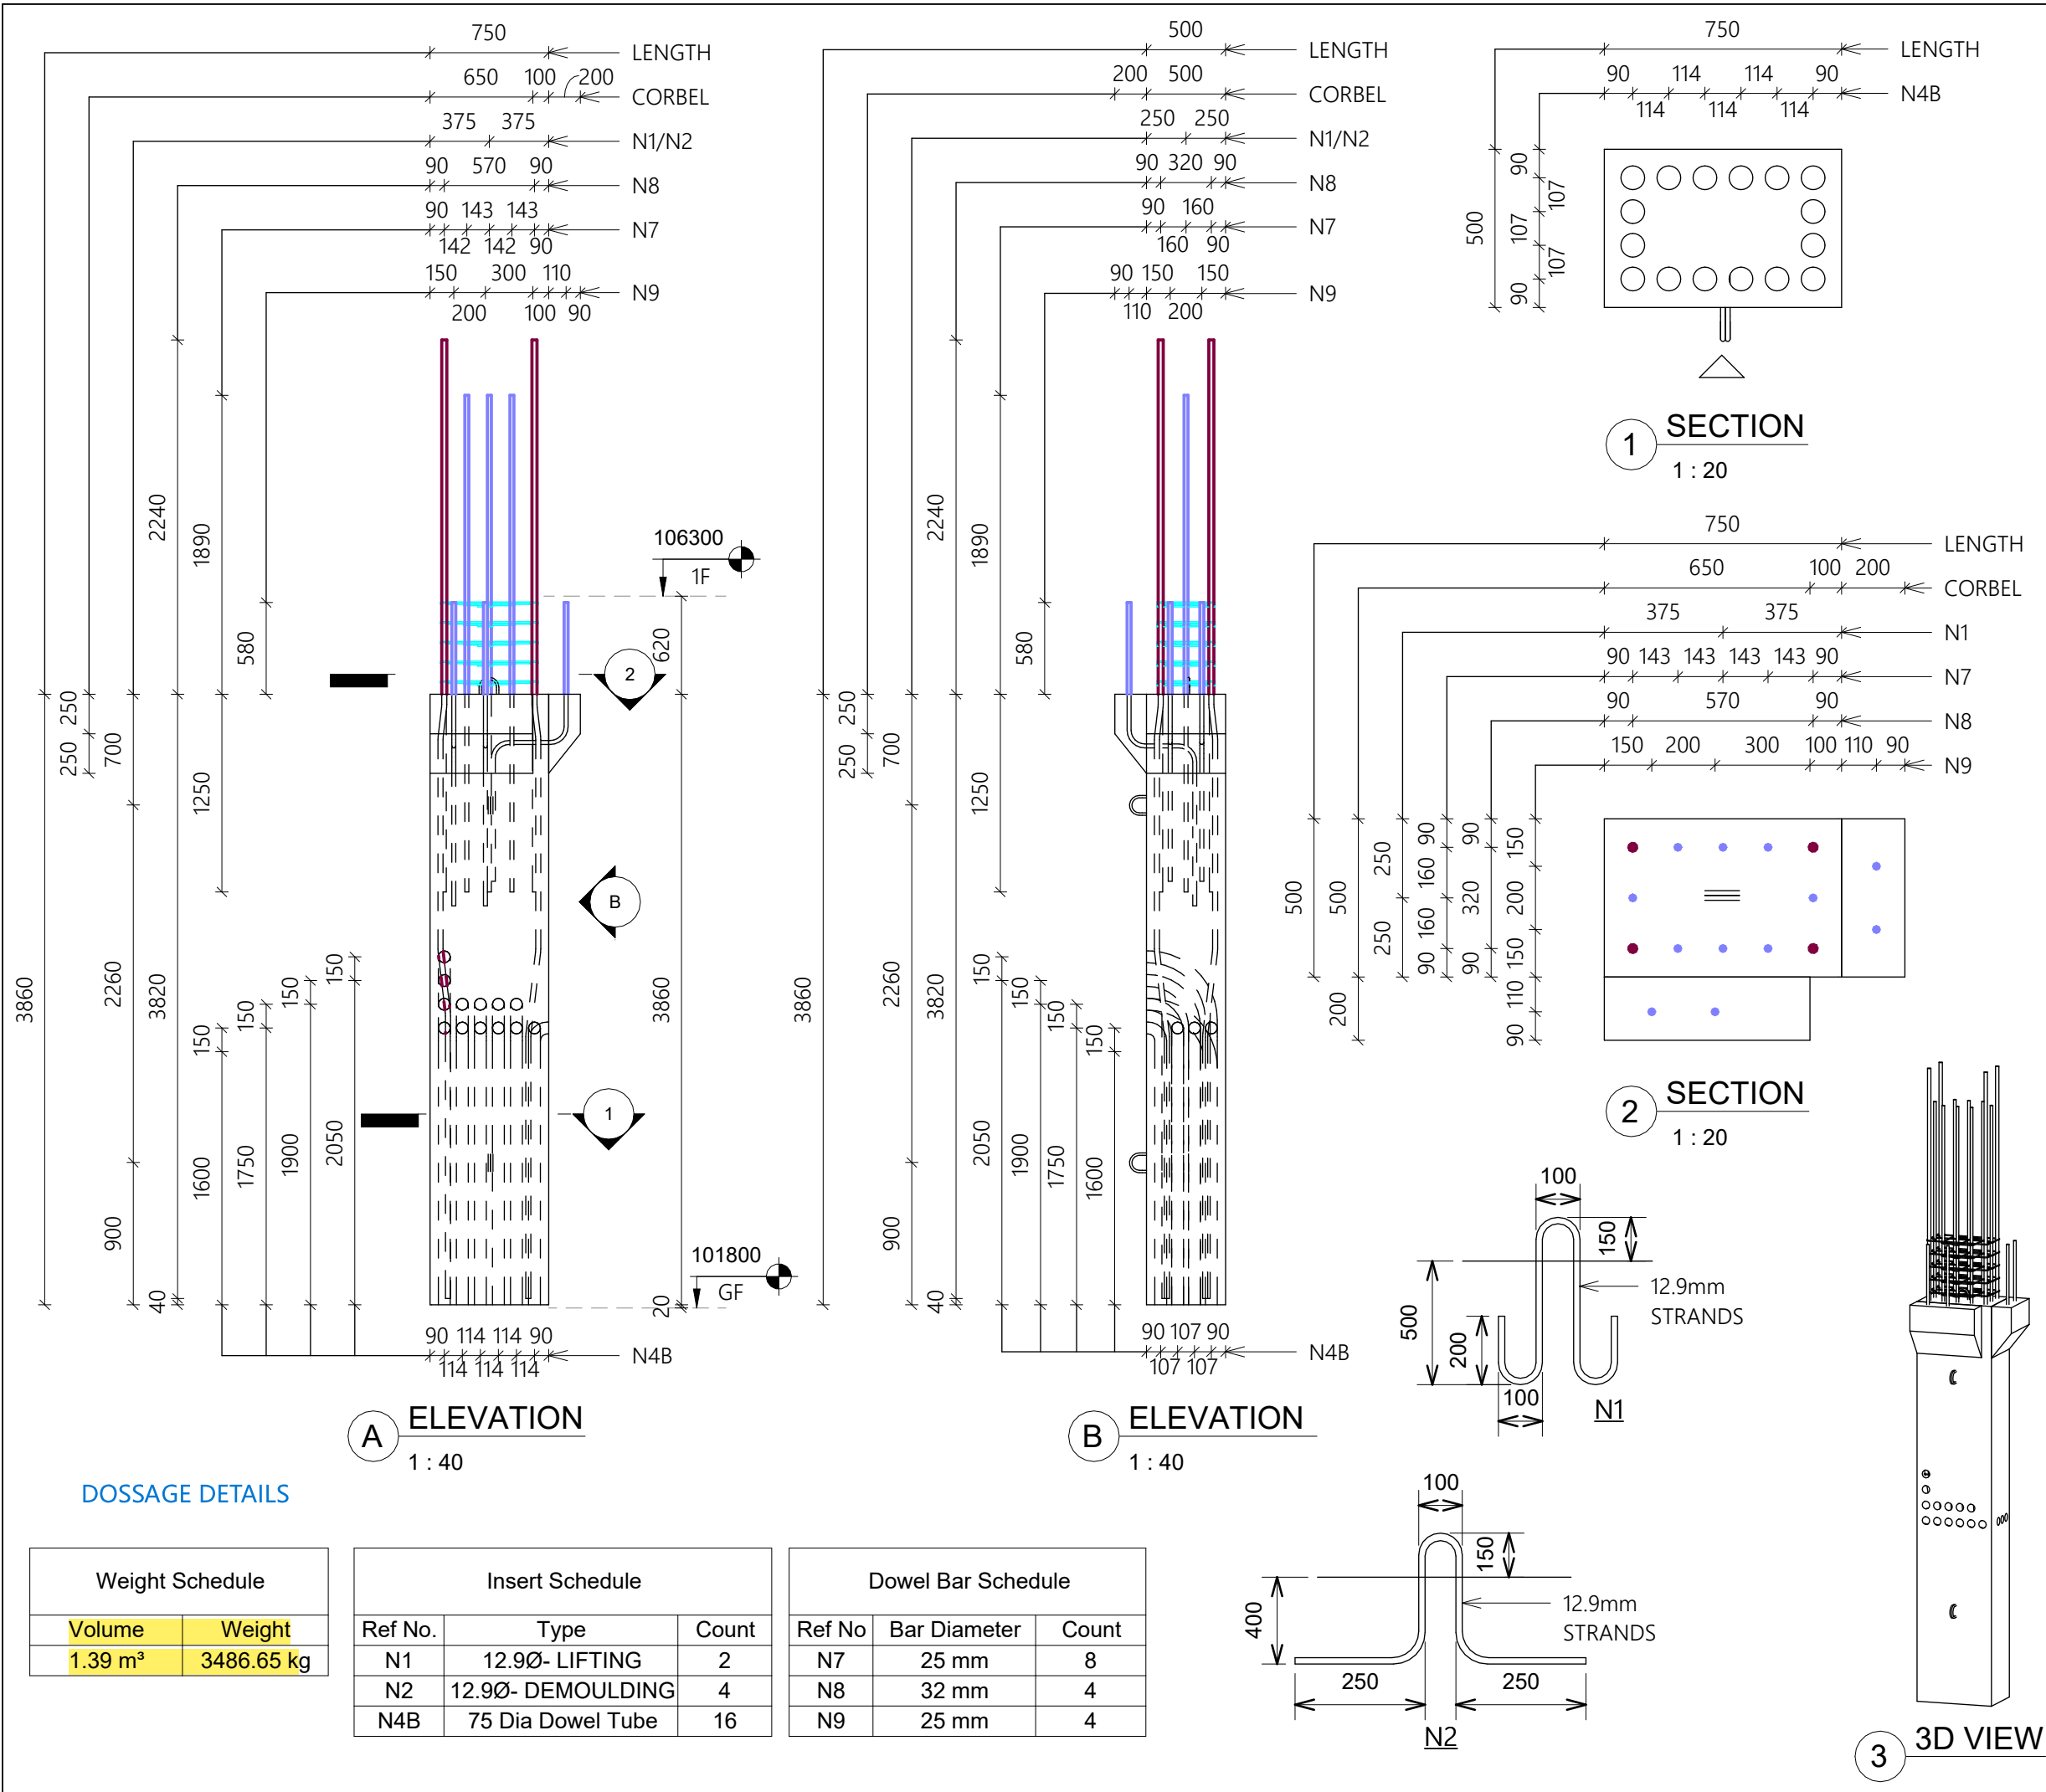

PROJECT :- SIFY BANGALORE				
GENERAL NOTES:				
GRADE OF CONCRETE	-	M50		
GRADE OF STEEL	-	Fe500		
STRIPPING STRENGTH	-	M25		
LIFTING,TRANSPORTATION AND ERECTION	-	M35		
COVER:				
COLUMN	-	40mm		
ALL DIMENSIONS ARE IN MM				
LEGENDS:				
ERECTION MARK	-			
CLIENT:				
EXCEL PRECAST SOLUTIONS PVT LTD				
#94, 4th MAIN,MCHS LAYOUT, JAKKUR ROAD, NEAR BHARAT SEVASHRAM, BENGALURU 560 064, KARNATAKA, INDIA. Mob No: +91 8904224014 Email: info@excelprecast.com Web: www.excelprecast.com				
STRUCTURAL CONSULTANT :-				
ES STRUCTURAL CONSULTANT				
No. A-241, South Extension street, N.G.O. 'A' Colony, Palayamkottai,Tirunelveli-627007. Ph.No:+91 9865803764				
DRAWING TITLE :- PC-GF-01-MOULD DRAWING				
JOB NO : ESP25047	DRAWN BY:-	GRS		
ELEMENT NO : : PC-GF-01	SHEET SIZE:-	A3		
SHEET NO : PC-GF-01(M)	REV.NO:-	0		
SCALE : As indicated	LEVEL :			